KT-03 · HIỆU CHỈNH TỪ KT-02


Mặt bằng nhà phố 4,2 × 18 m

2 tầng Trệt + Lầu **Tầng cao** trệt 3,78 m · lầu 3,6 m **Nền trệt** cao hơn mặt đường 0,32 m **Tường** 100 mm

Kích thước theo tim tường, đơn vị mét Bản để xem, không dùng xin phép/thi công

Tường 100 mm · Cửa đi (cung mở) · Cửa sổ (3 nét) · Hành lang / lối đi 1,0 m · Khu phơi (lộ thiên)
Ban công / lan can · Chiều lên thang · Vị trí mặt cắt A–A · Kích thước (m)

Tầng trệt 0,6 + 5,4 + 2,8 + 3,7 + 4,0 + 1,5 = 18,0 m

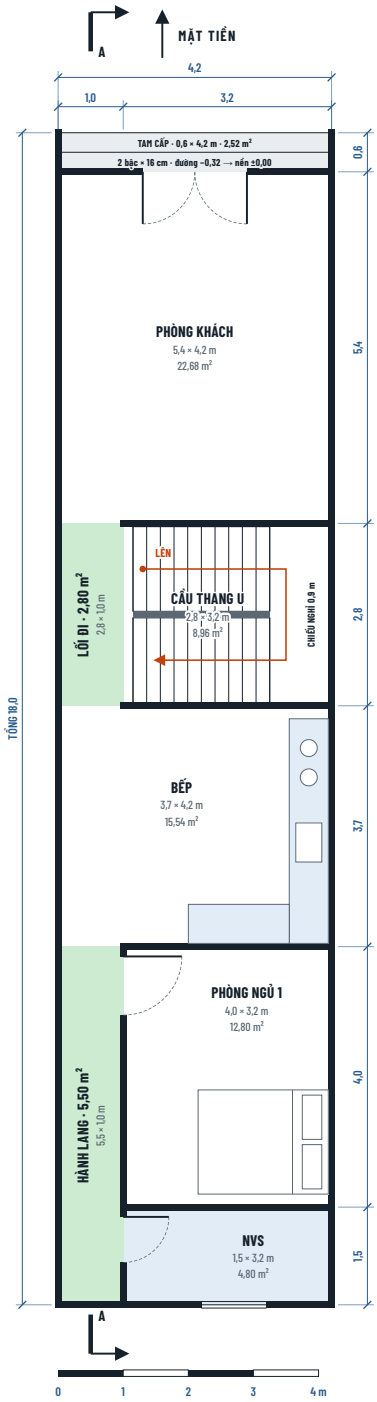

BẢNG THỐNG KÊ TẦNG TRỆT

PHÒNG	DÀI (M)	RỘNG (M)	DIỆN TÍCH (M²)
Tam cấp	0,6	4,2	2,52
Phòng khách	5,4	4,2	22,68
Lối đi	2,8	1,0	2,80
Cầu thang U	2,8	3,2	8,96
Bếp	3,7	4,2	15,54
Phòng ngủ 1	4,0	3,2	12,80
NVS	1,5	3,2	4,80
Hành lang	5,5	1,0	5,50
Thân nhà	**18,0**	**4,2**	**75,60**


ĐẠT Tổng chiều dài: 0,6 + 5,4 + 2,8 + 3,7 + 4,0 + 1,5 = 18,0 m

ĐẠT Tổng diện tích thân nhà 75,60 m² = 18,0 × 4,2 (không chồng, không hở)

ĐẠT Lõi thang x = 6,0–8,8, y = 1,0–4,2 trùng với tầng lầu

ĐẠT Thang 22 bậc × 17,2 cm (≤ 17,5) = 3,78 m = cao tầng trệt; vế 11 bậc dài 2,10 + chiếu nghỉ 0,90 = 3,00 m ≤ lòng 3,10 m

Tầng lầu (1,2) + 2,0 + 4,0 + 2,8 + 6,0 + 1,6 + 1,6 = 18,0 m

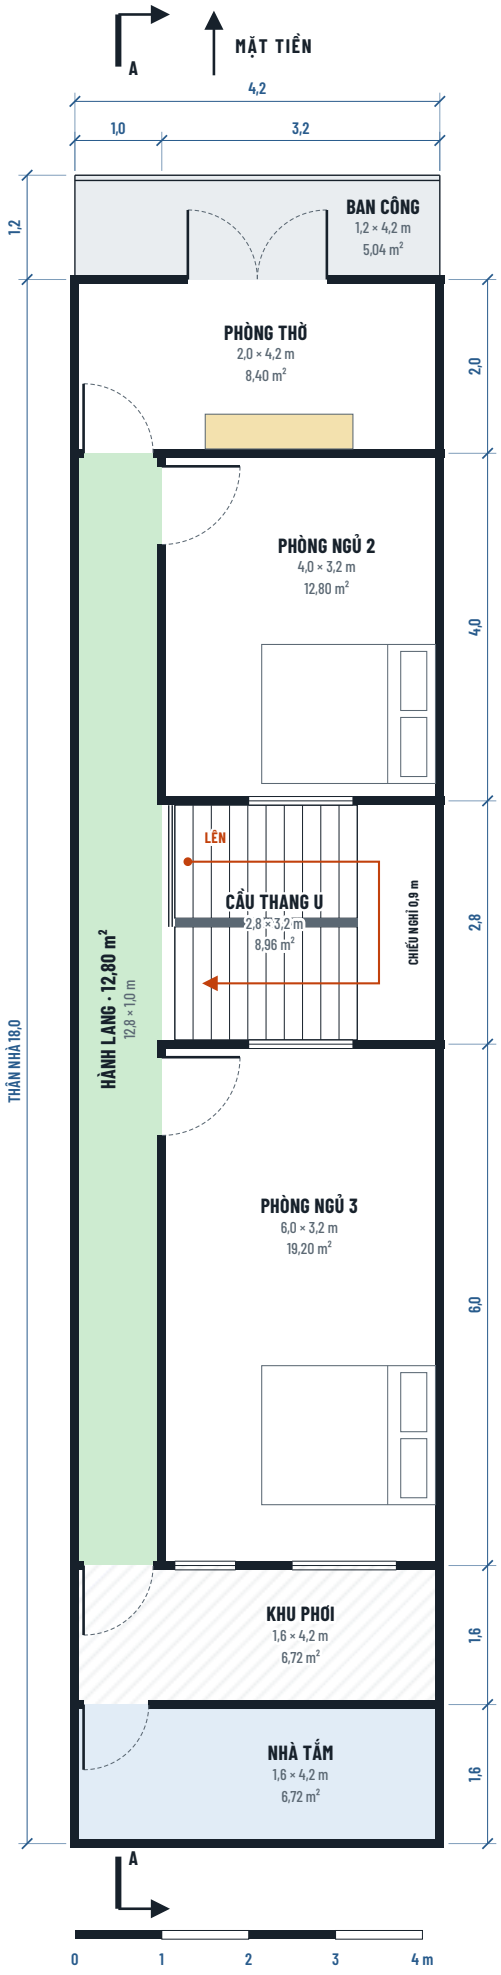

BẢNG THỐNG KÊ TẦNG LẦU

PHÒNG	DÀI (M)	RỘNG (M)	DIỆN TÍCH (M^2)
Ban công	1,2	4,2	5,04
Phòng thờ	2,0	4,2	8,40
Phòng ngủ 2	4,0	3,2	12,80
Cầu thang U	2,8	3,2	8,96
Phòng ngủ 3	6,0	3,2	19,20
Hành lang	12,8	1,0	12,80
Khu phơi	1,6	4,2	6,72
Nhà tắm	1,6	4,2	6,72
Thân nhà	**18,0**	**4,2**	**75,60**
Kể cả ban công			**80,64**


ĐẠT Tổng chiều dài: 2,0 + 4,0 + 2,8 + 6,0 + 1,6 + 1,6 = 18,0 m

ĐẠT Tổng diện tích thân nhà 75,60 m^2 = 18,0 × 4,2 (không chồng, không hở)

ĐẠT Lõi thang x = 6,0–8,8, y = 1,0–4,2 trùng với tầng trệt

ĐẠT Thang 22 bậc × 17,2 cm (≤ 17,5) = 3,78 m = cao tầng trệt; vế 11 bậc dài 2,10 + chiếu nghỉ 0,90 = 3,00 m ≤ lòng 3,10 m

Mặt cắt A–A cắt dọc nhà qua hành lang (y = 0,5 m), nhìn về phía tường hông y = 4,2

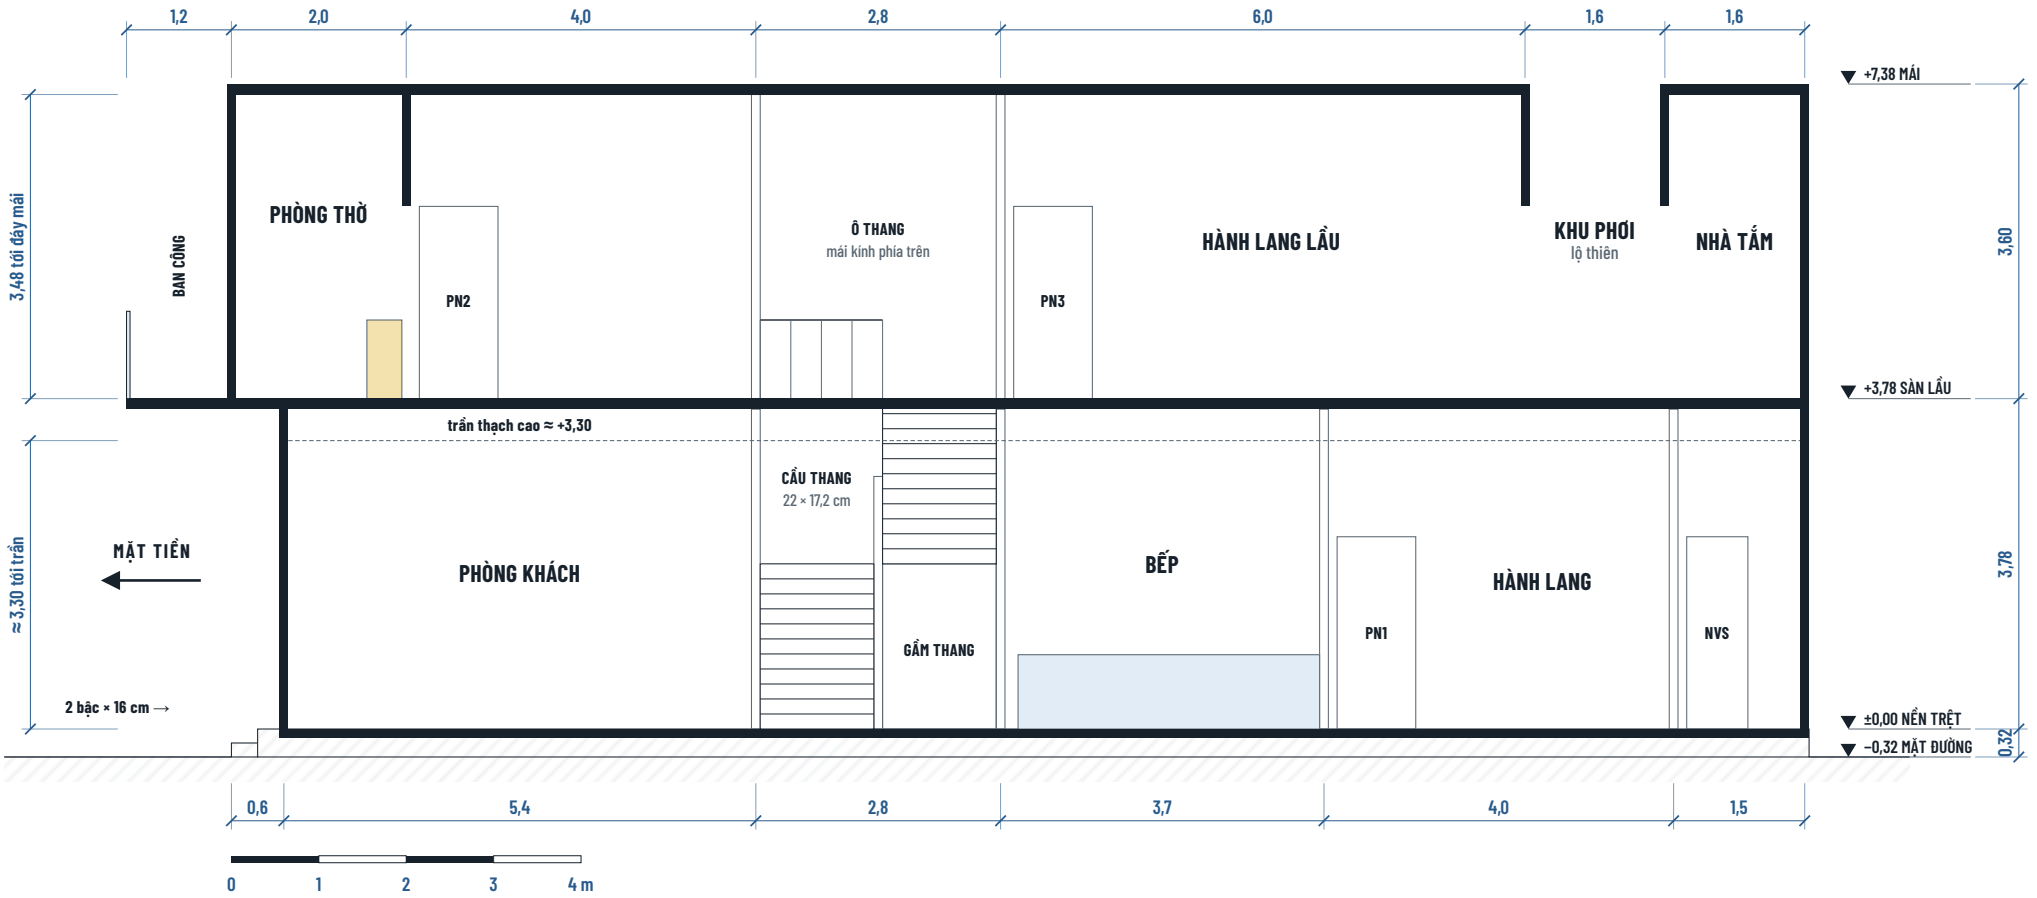

Tô đen: phần bị cắt (tường, sàn, mái). Nét mảnh: thấy phía sau mặt cắt. Giả định: sàn và mái bê tông dày 12 cm, cửa đi cao 2,2 m, lan can ban công 1,0 m, lan can ô thang 0,9 m, mái bằng chưa có tường chắn mái.

HIỆU CHỈNH LẦN 2

1. **PN3 thêm cửa sổ 1,2 m** (y = 2,5–3,7) ra khu phơi. Để cửa sổ thông ra ngoài trời, khu phơi đổi thành dải 1,6 m chạy hết bề ngang, giáp toàn bộ vách sau PN3. Nhà tắm 1,6 × 4,2 m nằm phía sau, vào qua khu phơi. Không mở cửa sổ ở tường hông y = 4,2 vì tường này thường giáp ranh nhà bên.
2. **Tầng trệt cao 3,78 m** (từ nền tới sàn lầu): thang 22 bậc × 17,2 cm (2 vế × 11 bậc), mặt bậc 21 cm. Trừ sàn bê tông, lớp lát (khoảng 17 cm) và trần thạch cao (khoảng 30 cm), từ nền tới trần còn khoảng 3,3 m.
3. **Tầng lầu cao 3,6 m** tính từ sàn lầu đến mái.
4. **Nền trệt cao hơn mặt đường 0,32 m** để nước mưa không tràn vào. Tam cấp 2 bậc × 16 cm, mỗi bậc sâu 0,3 m, nằm trong ranh đất ở x = 0–0,6. Tường mặt tiền và cửa chính lùi vào x = 0,6, nên phòng khách còn 5,4 × 4,2 m (22,68 m^2). Sàn lầu và ban công phía trên che mưa cho tam cấp. Nếu dắt xe máy vào nhà: 0,6 m quá ngắn để làm dốc cố định (dốc khoảng 28°), nên dùng cầu dắt xe tháo rời.

CHỖ LỆCH SO VỚI FILE KT-02 VÀ CÁCH XỬ LÝ

1. **Bề ngang phòng "rộng hết bề ngang".** File ghi 4,0 m (Phòng khách 24,0 m^2, Bếp 14,8 m^2, Phòng thờ 8,0 m^2, Ban công 4,8 m^2). Thông số tính theo tim tường nên bản này dùng bề ngang 4,2 m (Bếp 15,54 m^2, Phòng thờ 8,40 m^2, Ban công 5,04 m^2).
2. **Rộng phòng ngủ 2,9 m bị trừ tường sai.** File lấy 4,2 – 1,0 – 0,3, nhưng phòng ngủ chỉ có 1 vách giáp hành lang và 1 tường ngoài. Theo tim tường là 3,2 m, thông thủy khoảng 3,1 m (không phải 2,9). Số 4,0 m và 6,0 m ghi kèm chữ "thông thủy" thực ra là tim tường; thông thủy là 3,9 m và 5,9 m. Bảng ở trên ghi theo tim tường.
3. **Cầu thang xoay hướng vế.** File vẽ vế thang chạy dọc nhà. Kiểu đó không lọt: lòng thang dọc nhà chỉ 2,7 m, trong khi vế 11 bậc cần 10 × 0,21 + chiếu nghỉ 0,9 = 3,00 m. Bản này cho vế thang chạy theo bề ngang (lòng 3,1 m), còn dư 0,1 m. Hai vế rộng 1,3 m, cùng mở ra hành lang. Lõi thang vẫn ở x = 6,0–8,8, trùng ở 2 tầng.
4. **Cửa sổ PN2, PN3 "ở vách giáp cầu thang".** File đặt ở tường hông (y = 4,2). Bản này đặt đúng trên vách x = 6,0 và x = 8,8. Cửa này chỉ lấy sáng gián tiếp qua lõi thang, nên cần giếng trời hoặc mái lấy sáng trên thang.
5. **Cửa sổ sau PN3 trong file nhìn vào nhà tắm.** Bản này cho cả 2 cửa sổ sau của PN3 nhìn ra khu phơi (xem mục hiệu chỉnh lần 2).
6. **"Hành lang chữ L" ở trệt.** Theo tọa độ, hành lang chạy thẳng y = 0–1,0 từ x = 12,5 đến 18,0 dọc PN1 và NVS (file cũng vẽ thẳng). Bản này vẽ thẳng.
7. **Chi tiết file có nhưng thông số không nêu.** Giữ: cửa phòng thờ ra hành lang, bàn thờ, cửa sổ sau NVS. Bỏ: cửa sổ tường hông phòng khách (tường hông nhà phố thường giáp nhà bên).
8. **Độ dốc thang.** Bậc cao 17,2 cm, mặt bậc 21 cm cho 2h + b ≈ 55 cm, dốc khoảng 39°, dốc hơn mức thoải mái 60–64 cm. Lòng thang 3,1 m chỉ cho mặt bậc tối đa 22 cm (10 × 0,22 + 0,9 = 3,10 m).

Tường ngoài 100 mm và ban công đua 1,2 m cần kiểm tra lại theo quy chuẩn và lộ giới. Hồ sơ xin phép phải do kiến trúc sư có chứng chỉ lập.