KT-03 · HIỆU CHỈNH TỪ KT-02


Mặt bằng nhà phố 4,2 × 18 m

2 tầng Trệt + Lầu **Tầng cao** trệt 3,78 m · lầu 3,6 m **Nền trệt** cao hơn mặt đường 0,32 m **Tường** 100 mm

Kích thước theo tim tường, đơn vị mét Bản để xem, không dùng xin phép/thi công

Tường 100 mm | Cửa đi (cung mở) | Cửa sổ (3 nét) | Hành lang / lối đi 1,0 m | Khu phơi (mái tấm lấy sáng) | Ban công / lan can | Chiều lên thang | Vị trí mặt cắt A–A | Kích thước (m)

Tầng trệt 0,6 + 5,4 + 2,8 + 3,7 + 4,0 + 1,5 = 18,0 m

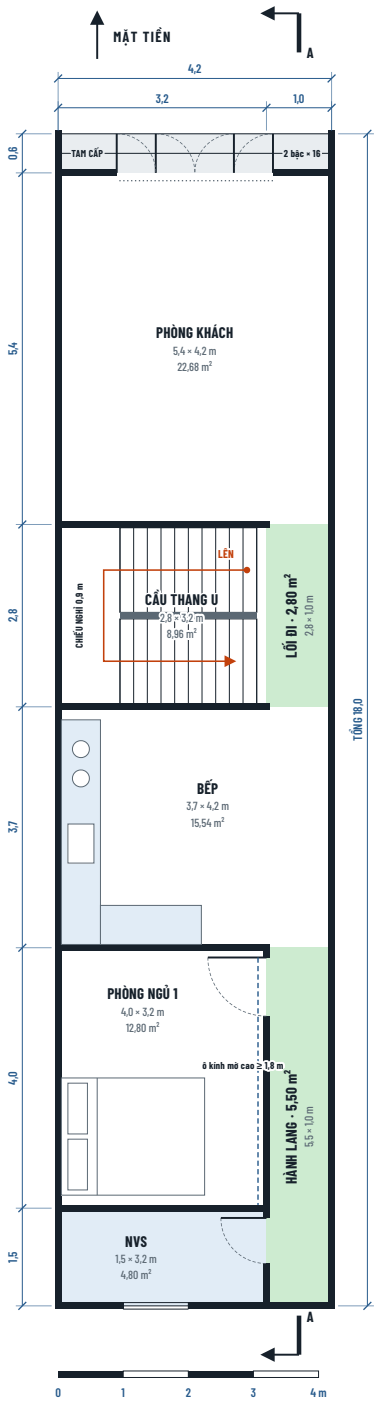

BẢNG THỐNG KÊ TẦNG TRỆT

PHÒNG	DÀI (M)	RỘNG (M)	DIỆN TÍCH (M²)
Tam cấp	0,6	4,2	2,52
Phòng khách	5,4	4,2	22,68
Lối đi	2,8	1,0	2,80
Cầu thang U	2,8	3,2	8,96
Bếp	3,7	4,2	15,54
Phòng ngủ 1	4,0	3,2	12,80
NVS	1,5	3,2	4,80
Hành lang	5,5	1,0	5,50
Thân nhà	**18,0**	**4,2**	**75,60**


ĐẠT Tổng chiều dài: 0,6 + 5,4 + 2,8 + 3,7 + 4,0 + 1,5 = 18,0 m

ĐẠT Diện tích trong ranh đất 75,60 m² = 18,0 × 4,2 (không chồng, không hở)

ĐẠT Lõi thang x = 6,0–8,8, y = 1,0–4,2 trùng với tầng lầu

ĐẠT Thang 22 bậc × 17,2 cm (≤ 17,5) = 3,78 m = cao tầng trệt; vế 11 bậc dài 2,10 + chiếu nghỉ 0,90 = 3,00 m ≤ lòng 3,10 m

Tầng lầu (ban công 1,2) + 2,0 + 4,0 + 2,8 + 6,0 + 3,2 = 18,0 m

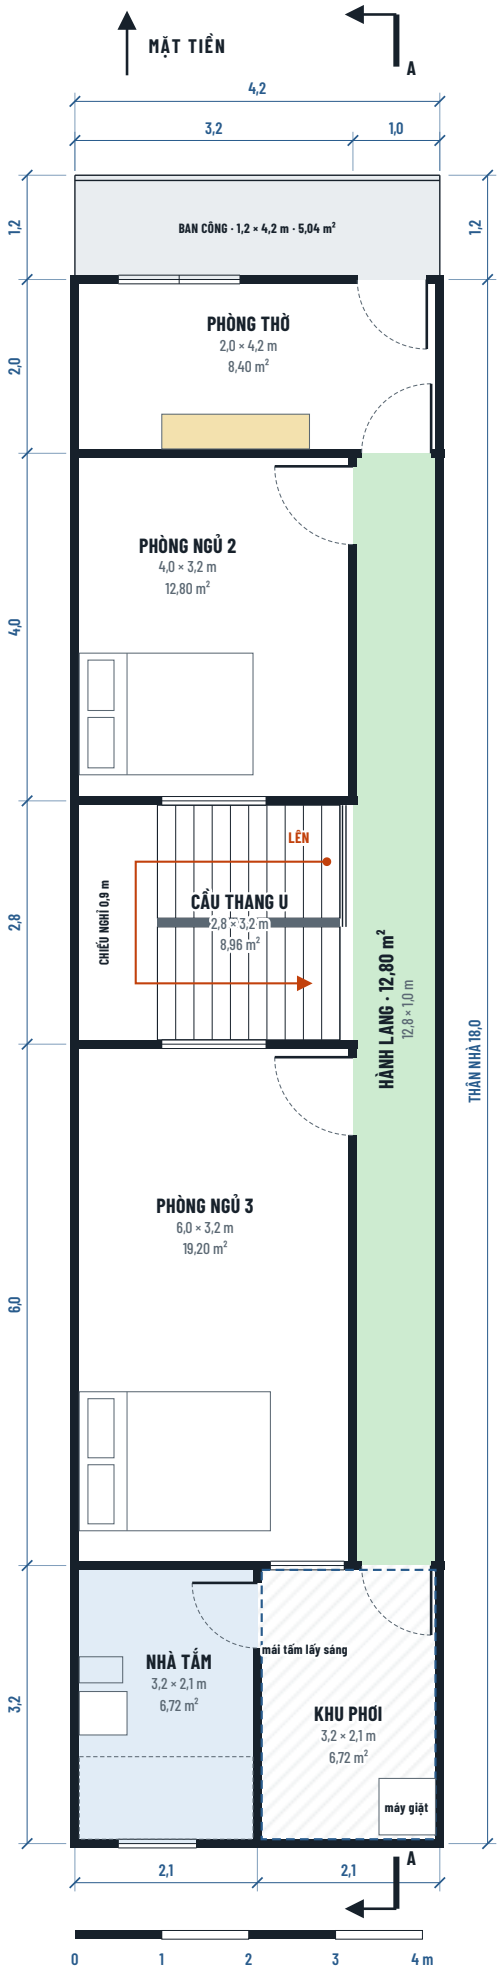

BẢNG THỐNG KÊ TẦNG LẦU

PHÒNG	DÀI (M)	RỘNG (M)	DIỆN TÍCH (M²)
Ban công	1,2	4,2	5,04
Phòng thờ	2,0	4,2	8,40
Phòng ngủ 2	4,0	3,2	12,80
Cầu thang U	2,8	3,2	8,96
Phòng ngủ 3	6,0	3,2	19,20
Hành lang	12,8	1,0	12,80
Khu phơi	3,2	2,1	6,72
Nhà tắm	3,2	2,1	6,72
Thân nhà	**18,0**	**4,2**	**75,60**
Nhô ra ngoài ranh đất			**5,04**
Tổng sàn kể cả phần nhô ra			**80,64**


ĐẠT Tổng chiều dài: 2,0 + 4,0 + 2,8 + 6,0 + 3,2 = 18,0 m

ĐẠT Diện tích trong ranh đất 75,60 m² = 18,0 × 4,2 (không chồng, không hở)

ĐẠT Lõi thang x = 6,0–8,8, y = 1,0–4,2 trùng với tầng trệt

ĐẠT Thang 22 bậc × 17,2 cm (≤ 17,5) = 3,78 m = cao tầng trệt; vế 11 bậc dài 2,10 + chiếu nghỉ 0,90 = 3,00 m ≤ lòng 3,10 m

Mặt cắt A-A cắt dọc nhà qua hành lang, nhìn về phía cầu thang; mặt tiền bên phải

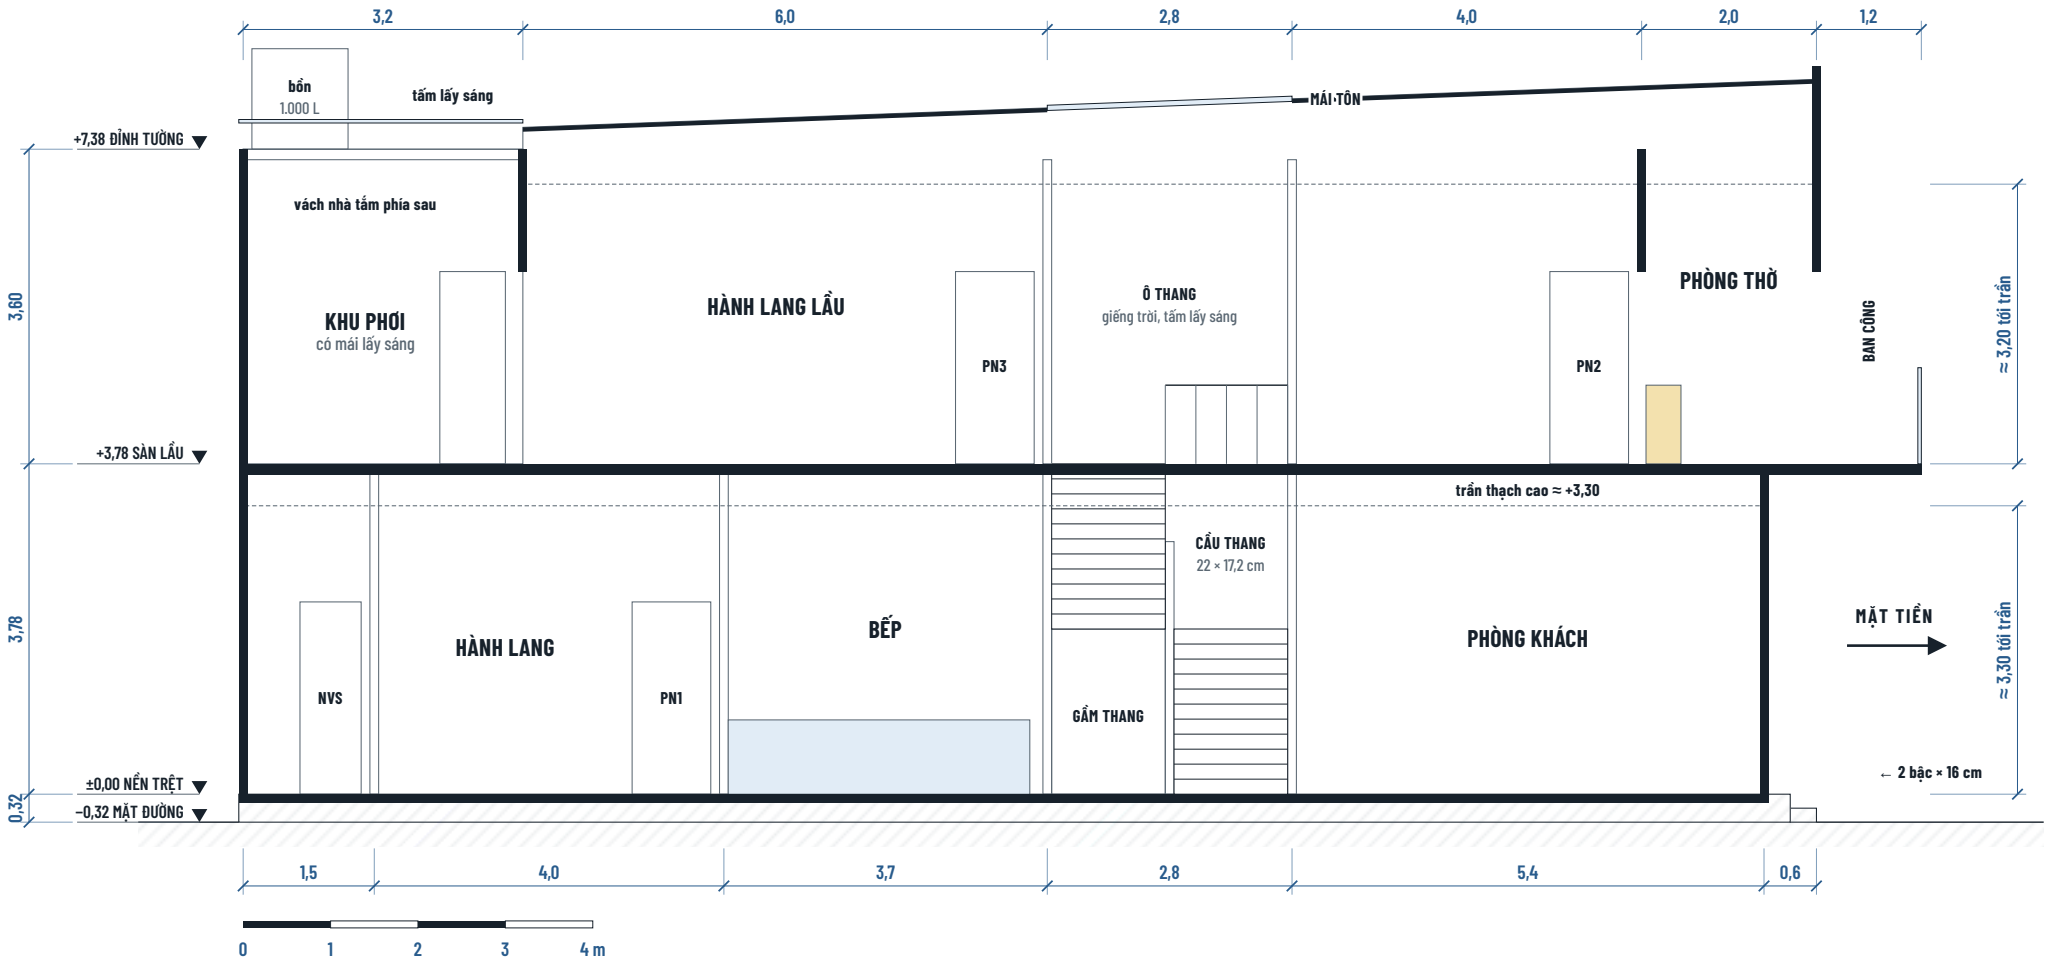

Tô đen: phần bị cắt (tường, sàn, mái). Nét mảnh: thấy phía sau mặt cắt. Giả định: sàn bê tông dày 12 cm, cửa đi cao 2,2 m, lan can ban công kính 1,1 m, lan can ô thang 0,9 m. Mái tôn cách nhiệt 3 lớp dốc từ mặt tiền ra sau (cao hơn đỉnh tường 0,8 m ở mặt tiền, 0,25 m ở x = 14,8); giếng trời trên thang lợp tấm lấy sáng kín; khu phơi lợp tấm lấy sáng cao hơn đỉnh tường 0,3 m, hở quanh mép; ô sàn bê tông trên nhà tắm lầu đặt bồn nước 1.000 L.

HIỆU CHỈNH LẦN 4 (THEO PHIẾU KHẢO SÁT LẦN 2, 01/11/2026 19H38)

1. **Xây đúng giấy phép, bỏ phần phòng thờ lấn ra:** sổ đỏ cho thấy ranh đất trùng mép tường mặt tiền, chủ đầu tư chọn xin phép ban công 1,2 m và xây đúng giấy phép. Tường mặt tiền lầu về lại x = 0; phòng thờ 2,0 × 4,2 m (8,40 m^2); ban công 1,2 × 4,2 m để hở, lan can kính cường lực 1,1 m. Mặt tiền lầu giữ cửa đi 1 cánh 0,8 m nhôm kính trong mở vào (phía hành lang) và cửa sổ 2 cánh 1,4 m mở hất ra ngoài, bệ 0,9 m, khung sắt bảo vệ phía trong.
2. **Cửa chính 4 cánh × 0,6 m mở ra ngoài** (tổng 2,4 m, y = 0,9–3,3): cánh quét gọn trong tam cấp 0,6 m, không lấn ra vỉa hè. Khung sắt bảo vệ đặt phía trong (nét chấm sau cửa).
3. **Khu phơi lợp tấm lấy sáng toàn bộ** thay cho mái che lối đi 1 m. Mái đặt cao hơn đỉnh tường khoảng 0,3 m, hở quanh mép để hơi nóng của 3 dàn nóng thoát ra. Máy giặt vẫn ở góc sau, không cần ô văng riêng.
4. **Giếng trời trên thang lợp tấm lấy sáng kín** thay cho mái tôn nâng hở hai bên. Kín thì không dột, không bụi nhưng hơi nóng dồn lên ô thang và hành lang lầu. Nên gắn thêm 1 quạt hút trên mái tôn cạnh giếng trời (loại chụp chống mưa) để hút hơi nóng ra; đi sẵn dây điện lên đó lúc xây.
5. **PN1 thêm ô kính mờ cao từ 1,8 m** ở vách hành lang và phía trên cửa đi (nét đứt xanh), lấy sáng gián tiếp từ hành lang.
6. **Giường cũ mang qua:** PN1 1,8 × 2,2 m; PN2 1,4 × 2,0 m; PN3 1,6 × 2,2 m. Cả 3 phòng đều kê vừa, còn lối đi trên 0,6 m.
7. **Giữ nguyên theo phiếu:** cửa sổ PN3 0,85 m; nhà tắm lầu tắm đứng vách kính, không bồn; ô sàn bê tông đặt bồn nước; dàn nóng như bản vẽ; mái tôn 3 lớp có PU.

HIỆU CHỈNH LẦN 3 (01/11/2026, ĐÃ THAY BẰNG LẦN 4 Ở MỤC 1)

1. **Khu phơi và nhà tắm lầu chia dọc:** khu phơi 3,2 × 2,1 m phía hành lang, nhà tắm 3,2 × 2,1 m có cửa sổ ra sau nhà, ô sàn bê tông phía trên đặt bồn nước. PN3 còn 1 cửa sổ 0,85 m ra khu phơi và cửa sổ trông vào lõi thang.
2. **Lộ giới 15 m** (vỉa hè 3,5 m + đường 8 m + vỉa hè 3,5 m): ban công được đua tối đa 1,2 m.

HIỆU CHỈNH LẦN 2

1. **PN3 thêm cửa sổ 1,2 m** (y = 2,5–3,7) ra khu phơi (lần 3 đã bỏ cửa này vì nhà tắm chuyển sang). Để cửa sổ thông ra ngoài trời, khu phơi đổi thành dải 1,6 m chạy hết bề ngang, giáp toàn bộ vách sau PN3. Nhà tắm 1,6 × 4,2 m nằm phía sau, vào qua khu phơi. Không mở cửa sổ ở tường hông y = 4,2 vì tường này thường giáp ranh nhà bên.
2. **Tầng trệt cao 3,78 m** (từ nền tới sàn lầu): thang 22 bậc × 17,2 cm (2 vế × 11 bậc), mặt bậc 21 cm. Trừ sàn bê tông, lớp lát (khoảng 17 cm) và trần thạch cao (khoảng 30 cm), từ nền tới trần còn khoảng 3,3 m.
3. **Tầng lầu cao 3,6 m** tính từ sàn lầu đến mái.
4. **Đảo bên cả nhà:** đứng ở cửa chính nhìn vào, hành lang và lối đi nằm bên trái, cầu thang và các phòng ngủ nằm bên phải. Tầng lầu đảo theo để lõi thang vẫn trùng nhau. Toạ độ y trong ghi chú tính từ tường hông bên phải (y = 0) sang bên trái (y = 4,2).
5. **Nền trệt cao hơn mặt đường 0,32 m** để nước mưa không tràn vào. Tam cấp 2 bậc × 16 cm, mỗi bậc sâu 0,3 m, nằm trong ranh đất ở x = 0–0,6. Tường mặt tiền và cửa chính lùi vào x = 0,6, nên phòng khách còn 5,4 × 4,2 m (22,68 m^2). Sàn lầu và ban công phía trên che mưa cho tam cấp. Nếu dắt xe máy vào nhà: 0,6 m quá ngắn để làm dốc cố định (dốc khoảng 28°), nên dùng cầu dắt xe tháo rời.

CHỖ LỆCH SO VỚI FILE KT-02 VÀ CÁCH XỬ LÝ

1. **Bề ngang phòng "rộng hết bề ngang".** File ghi 4,0 m (Phòng khách 24,0 m^2, Bếp 14,8 m^2, Phòng thờ 8,0 m^2, Ban công 4,8 m^2). Thông số tính theo tim tường nên bản này dùng bề ngang 4,2 m (Bếp 15,54 m^2, Phòng thờ 8,40 m^2, Ban công 5,04 m^2).
2. **Rộng phòng ngủ 2,9 m bị trừ tường sai.** File lấy 4,2 – 1,0 – 0,3, nhưng phòng ngủ chỉ có 1 vách giáp hành lang và 1 tường ngoài. Theo tim tường là 3,2 m, thông thủy khoảng 3,1 m (không phải 2,9). Số 4,0 m và 6,0 m ghi kèm chữ "thông thủy" thực ra là tim tường; thông thủy là 3,9 m và 5,9 m. Bảng ở trên ghi theo tim tường.

3. **Cầu thang xoay hướng vế.** File vẽ vế thang chạy dọc nhà. Kiểu đó không lọt: lòng thang dọc nhà chỉ 2,7 m, trong khi vế 11 bậc cần 10 × 0,21 + chiếu nghỉ 0,9 = 3,00 m. Bản này cho vế thang chạy theo bề ngang (lòng 3,1 m), còn dư 0,1 m. Hai vế rộng 1,3 m, cùng mở ra hành lang. Lõi thang vẫn ở x = 6,0–8,8, trùng ở 2 tầng.
4. **Cửa sổ PN2, PN3 "ở vách giáp cầu thang".** File đặt ở tường hông (y = 4,2). Bản này đặt đúng trên vách x = 6,0 và x = 8,8. Cửa này chỉ lấy sáng gián tiếp qua lõi thang, nên cần giếng trời hoặc mái lấy sáng trên thang.
5. **Cửa sổ sau PN3 trong file nhìn vào nhà tắm.** Bản này cho cả 2 cửa sổ sau của PN3 nhìn ra khu phơi (xem mục hiệu chỉnh lần 2).
6. **"Hành lang chữ L" ở trệt.** Theo tọa độ, hành lang chạy thẳng y = 0–1,0 từ x = 12,5 đến 18,0 dọc PN1 và NVS (file cũng vẽ thẳng). Bản này vẽ thẳng.
7. **Chi tiết file có nhưng thông số không nêu.** Giữ: cửa phòng thờ ra hành lang, bàn thờ, cửa sổ sau NVS. Bỏ: cửa sổ tường hông phòng khách (tường hông nhà phố thường giáp nhà bên).
8. **Độ dốc thang.** Bậc cao 17,2 cm, mặt bậc 21 cm cho 2h + b ≈ 55 cm, dốc khoảng 39°, dốc hơn mức thoải mái 60–64 cm. Lòng thang 3,1 m chỉ cho mặt bậc tối đa 22 cm (10 × 0,22 + 0,9 = 3,10 m).

Lộ giới 15 m nên ban công được đua 1,2 m (điều kiện theo QCVN 01:2021 xem trang Cột và điện). Tường ngoài 100 mm cần kiểm tra lại theo quy chuẩn. Từ 01/7/2026, Luật Xây dựng 2025 miễn giấy phép cho nhà ở riêng lẻ dưới 7 tầng, dưới 500 m^2 sàn, trừ khu vực có quy chế quản lý kiến trúc; cần hỏi UBND phường/xã xem lô đất có thuộc diện miễn không. Bản vẽ xin phép hoặc bản vẽ thi công nên do đơn vị thiết kế có chứng chỉ lập.